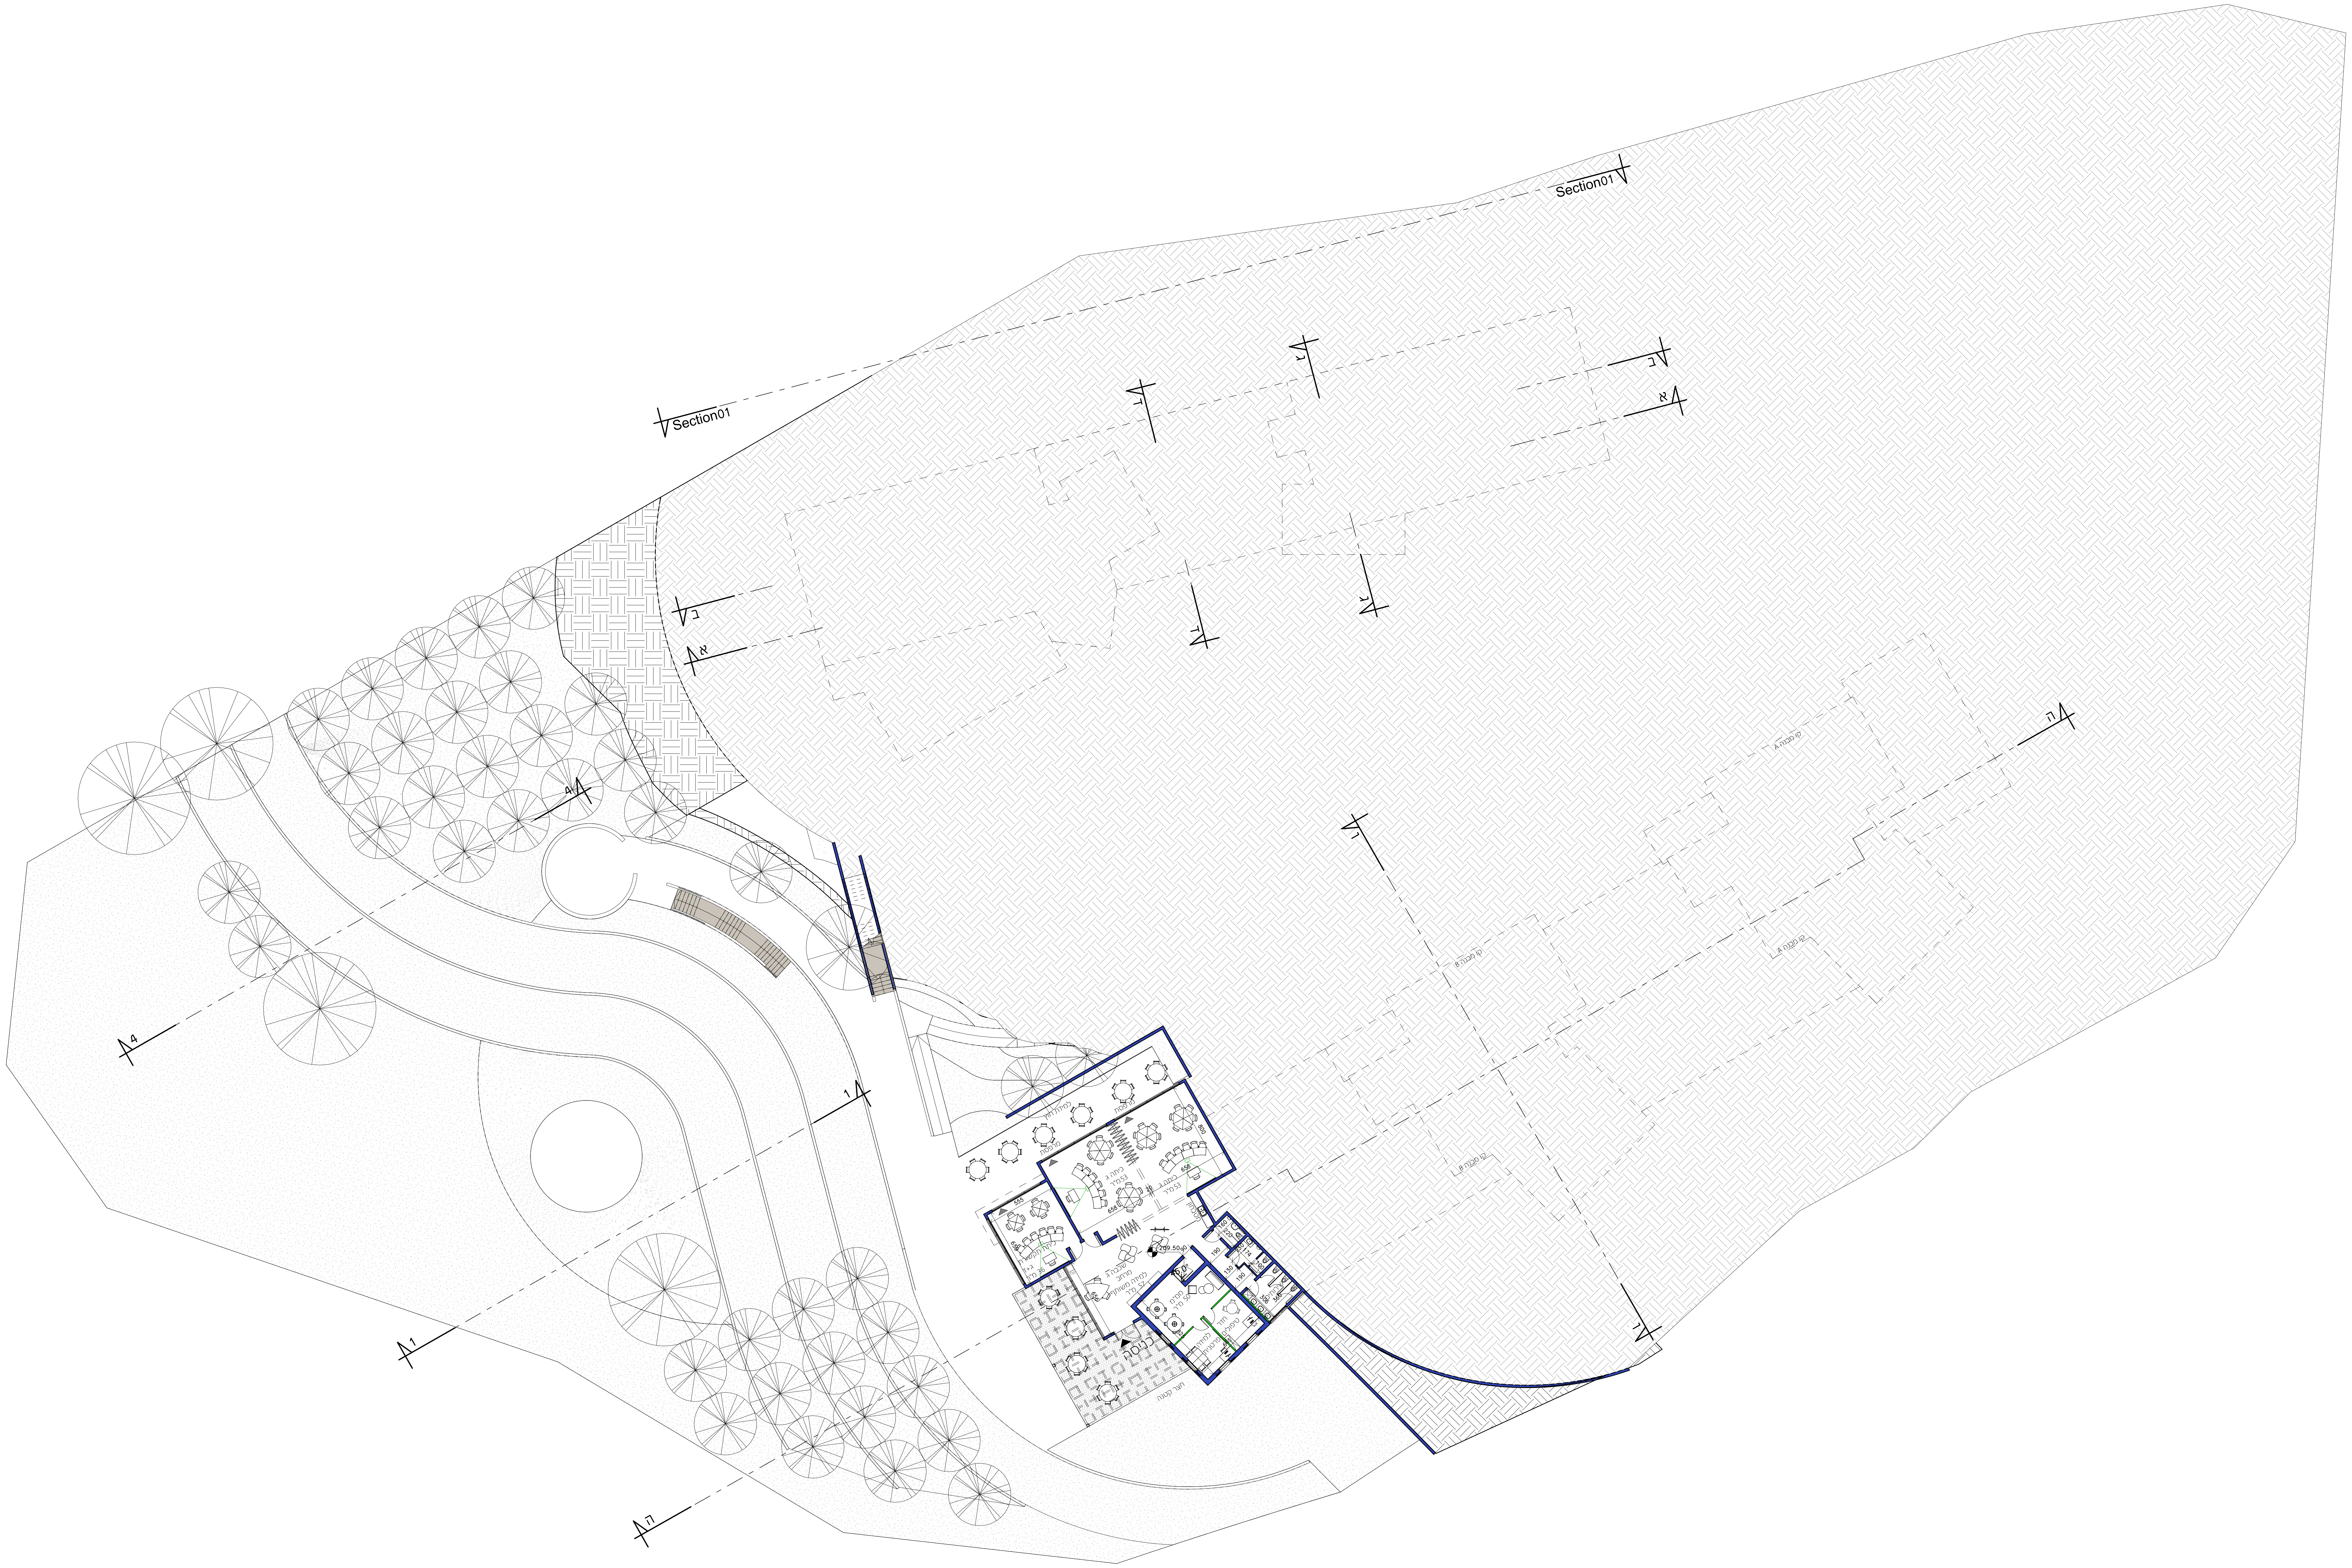
Section01
Section01
א
ב
ג
ד
ה
מרפסת
מרפסת
למידת חוץ
כיתה ג
53 מ"ר
כיתה ג
53 מ"ר
כיתת תקשורת
ג+T
36 מ"ר
שכבה ג
מרחב
למידה משותף
57 מ"ר
ממ"מ
50 מ"ר
חדר
טיפולים
למידה
פרטנית
מטבחון
שירותים
כניסה
חצר קטנה
-209.50
45.0°
555
658
658
658
656
650
800
20
160
220
190
130
190
174
306
360