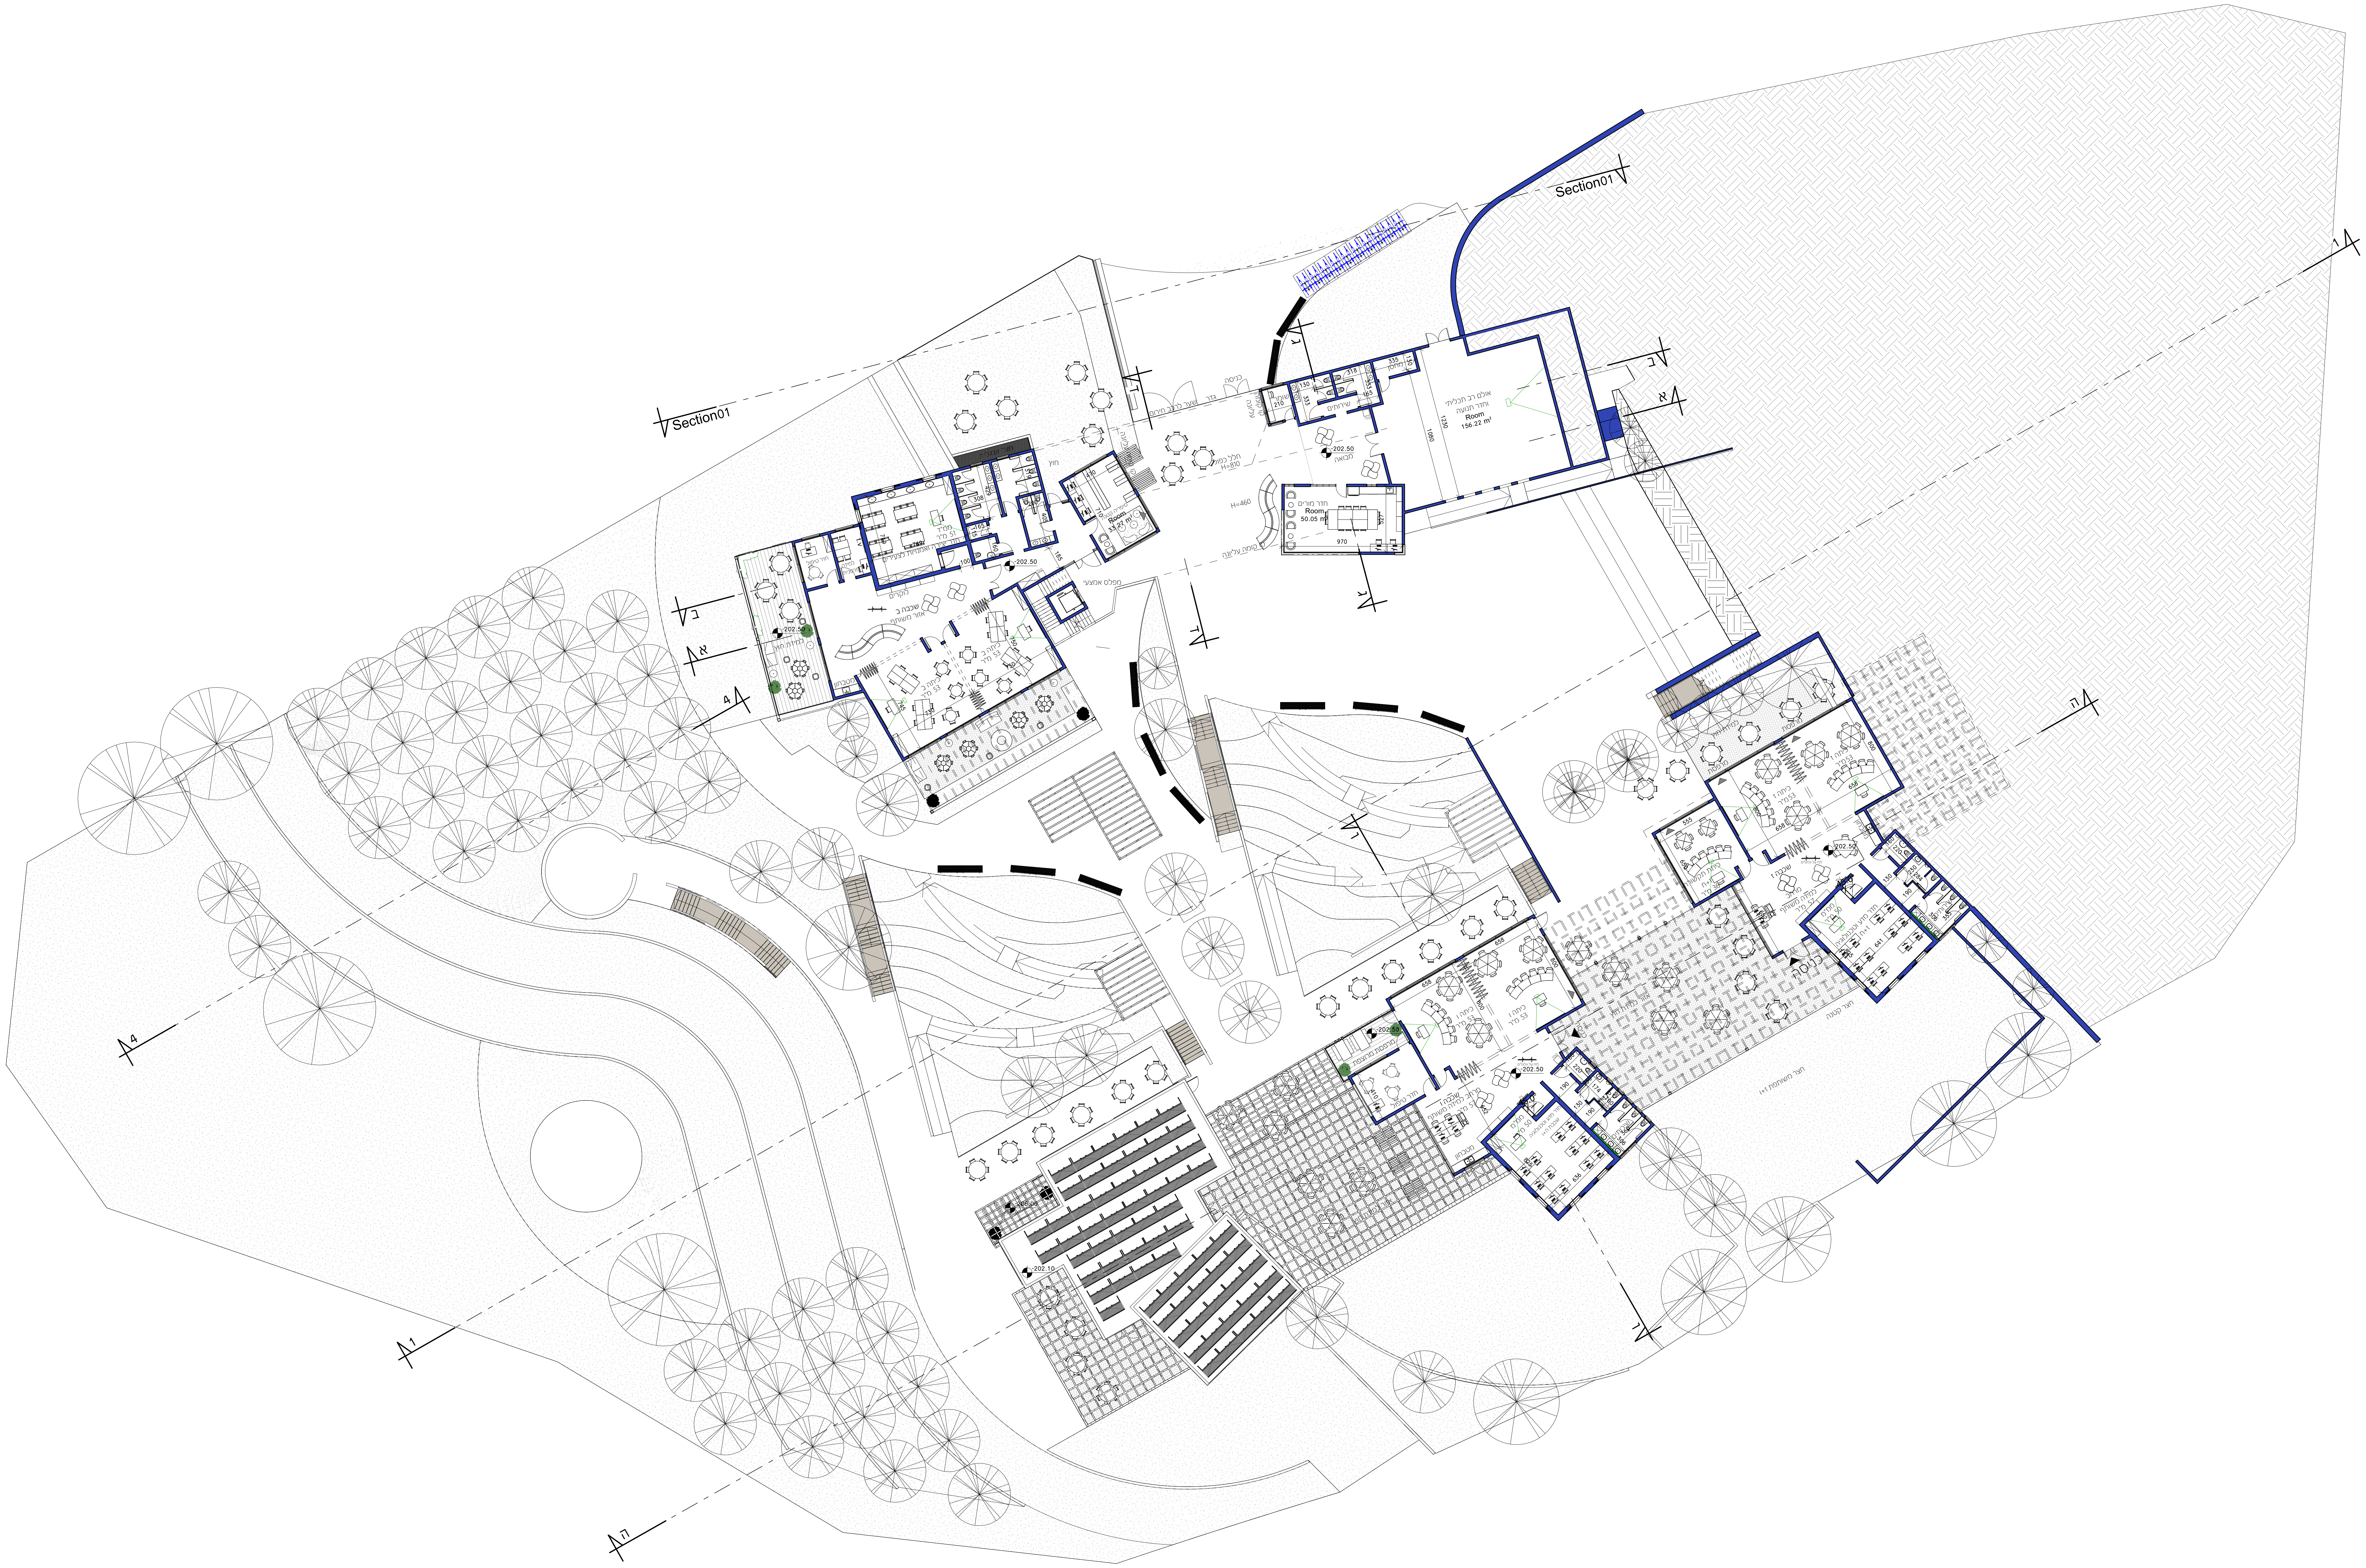
Section01
Section01
אולם רב תכליתי
וחדר תנועה
Room
156.22 m²
1230
1080
מחסן
335
130
שירותים
318
333
165
130
333
שומר
210
כניסה
גדר
שער לרכב חירום
מבואה
-202.50
חלל כפול
H=810
H=460
חדר מורים
Room
50.05 m²
970
527
קו קומה עליונה
מפלס אמצעי
ספריה קטנה
Room
33.27 m²
470
710
חוץ
ממ"ד
51 מ"ר
חדר יצירה ואמנויות לצעירים
769
308
429
165
115
160
200
405
185
100
-202.50
לוקרים
שכבה ב
אזור משותף
חדר טיפול
למידה פרטנית
t.v
למידת חוץ
-202.50
מטבחון
כיתה ב
53 מ"ר
כיתה ב
53 מ"ר
750
730
745
730
כיתה ז
53 מ"ר
כיתה ז
53 מ"ר
800
658
מרפסת
למידת חוץ
כיתת תקשורת
ח+ז
36 מ"ר
555
650
שכבה ז
מרחב
למידה משותף
57 מ"ר
-202.50
לוח על גלגלים
חדר מדע וטכנולוגיה
ז+ח
ממ"מ
50 מ"ר
641
485
שירותים
306
355
160
220
230
284
130
190
כניסה
אזור למידת חוץ
חצר קטנה
חצר משותפת ז+ח
כיתה ו
53 מ"ר
כיתה ו
53 מ"ר
658
800
מרפסת מרוצפת
חדר טיפול
410
שכבה ו
מרחב למידה משותף
57 מ"ר
652
-202.50
מטבחון
חדר מדע וטכנולוגיה
שכבת ה+ו
ממ"מ
50 מ"ר
825
636
220
174
190
130
190
160
שירותים
360
306
-206.00
-202.10
אזור למידת חוץ
א
א
ב
ב
ג
ג
ד
ד
ה
ה
1
1
4
4